SINTESI OPERATIVA PER PROFESSIONISTI


Guida Pratica all'Allegato III (D.P.R. 151/2011)

La documentazione tecnica per la prevenzione incendi: dal progetto alla SCIA.



NotebookLM

L’Ecosistema Documentale: Il Ciclo di Vita

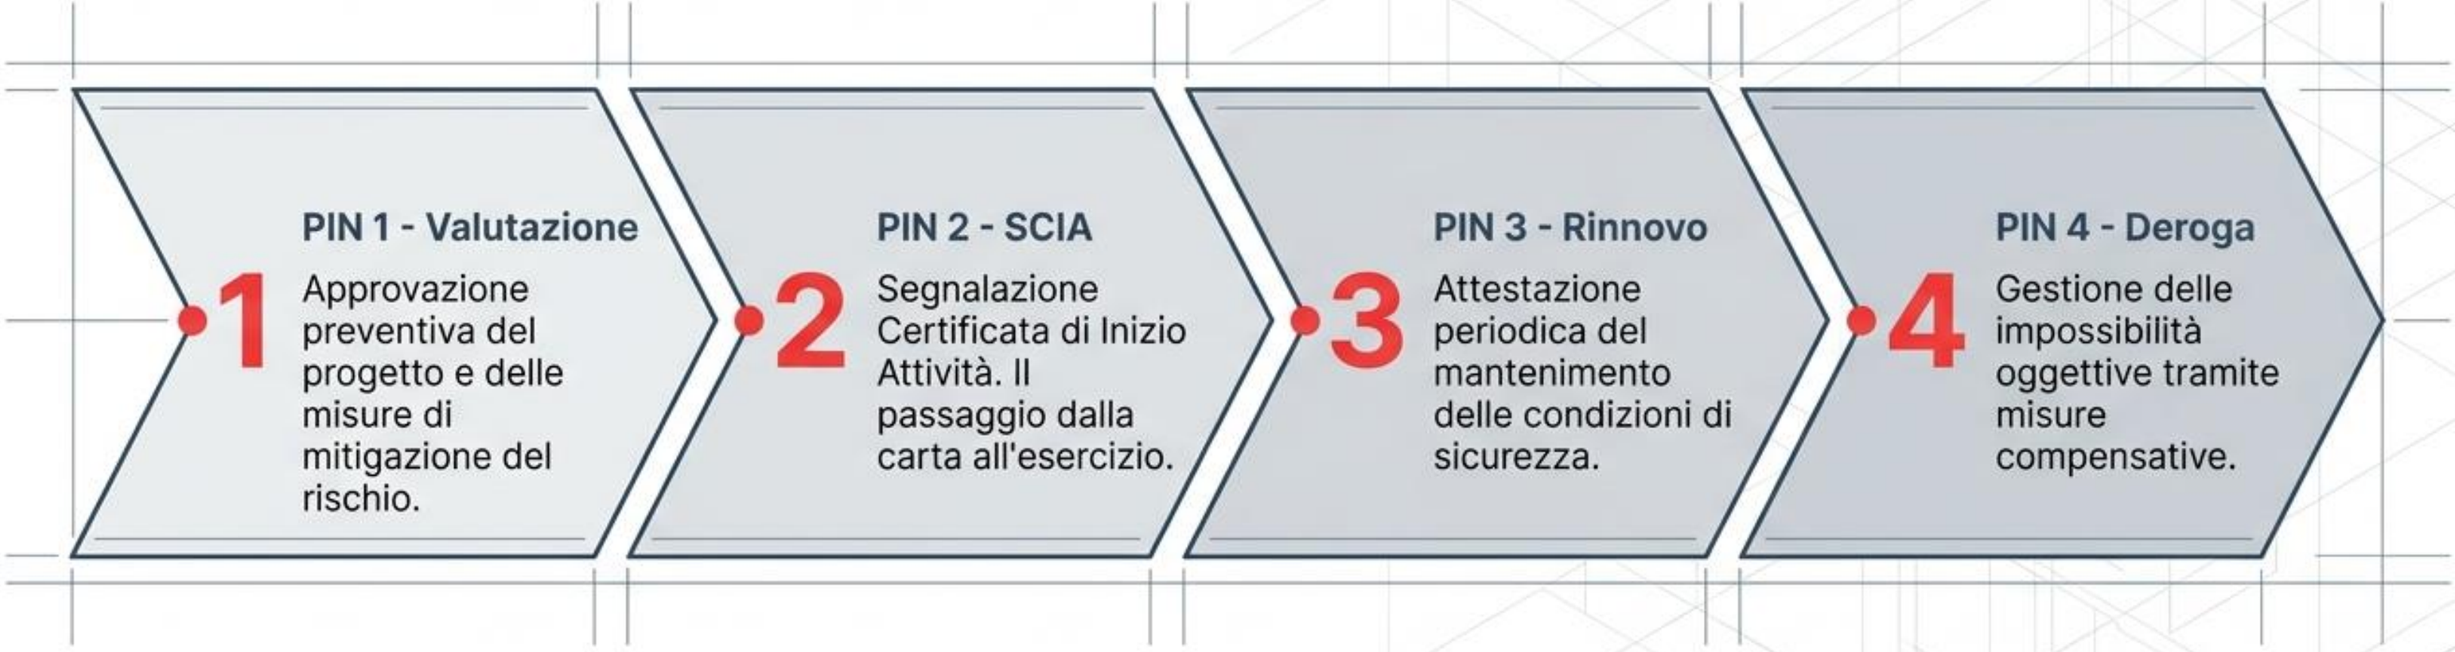

NotebookLM

Matrice degli Adempimenti Tecnici

Tipo di Istanza	Relazione Tecnica	Elaborati Grafici	Asseverazione Tecnico	Cert. Strutture (REI)	Cert. Impianti (DiCo)	Cert. Materiali/Prodotti
PIN 1 (Valutazione)	✓	✓	–	–	–	–
PIN 2 (SCIA)	–	–	✓	✓	✓	✓
PIN 3 (Rinnovo)	Dichiarazione Responsabile	Se aggiornati	✓	–	–	–
PIN 4 (Deroga)	Analisi Rischio + Misure	Eventuale	–	–	–	–

Insight: La SCIA (PIN 2) rappresenta il picco del carico documentale, richiedendo la transizione dalle ipotesi progettuali alle certificazioni as-built.

NotebookLM

PIN 1 – Valutazione del Progetto


IL CONCETTO



Relazione Tecnica

La dimostrazione analitica di come il progetto mitiga il rischio d'incendio, dalle lavorazioni svolte fino alle specifiche misure di protezione adottate.

LA GEOMETRIA

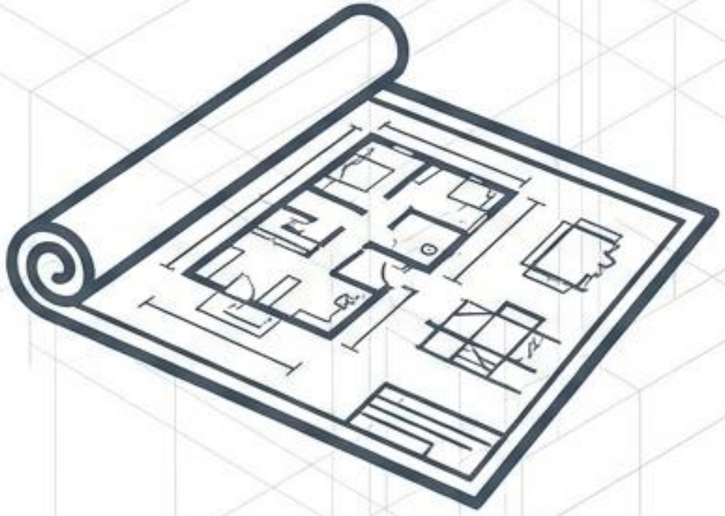

Elaborati Grafici

La traduzione spaziale della relazione tecnica. Piante, sezioni e schemi che localizzano fisicamente ogni singola misura di prevenzione e protezione.

NotebookLM

Anatomia della Relazione Tecnica



Attività e Lavorazioni

Numero e descrizione da Allegato I; lavorazioni svolte.



Sostanze Pericolose

Quantità, caratteristiche e specifiche modalità di stoccaggio.



Condizioni Ambientali

Ubicazione, accessibilità e viabilità dell'area.



Valutazione del Rischio

Criteri adottati per la stima del rischio incendio.



Misure di Protezione

Resistenza al fuoco, compartimentazione, vie timentazione, vie d'esodo, impianti attivi e gestione emergenza.



Riferimenti Normativi

Regole tecniche verticali e Codice di prevenzione incendi.

NotebookLM


L’Ingegneria Visiva: Elaborati Grafici

Planimetria (≥ 1:2000)

Edifici limitrofi, viabilità, idranti esterni e accessi VVF.

Piante (≥ 1:200)

Layout, destinazioni d’uso. Dettaglio critico: percorsi di esodo (larghezze/lunghezze), uscite, estintori.

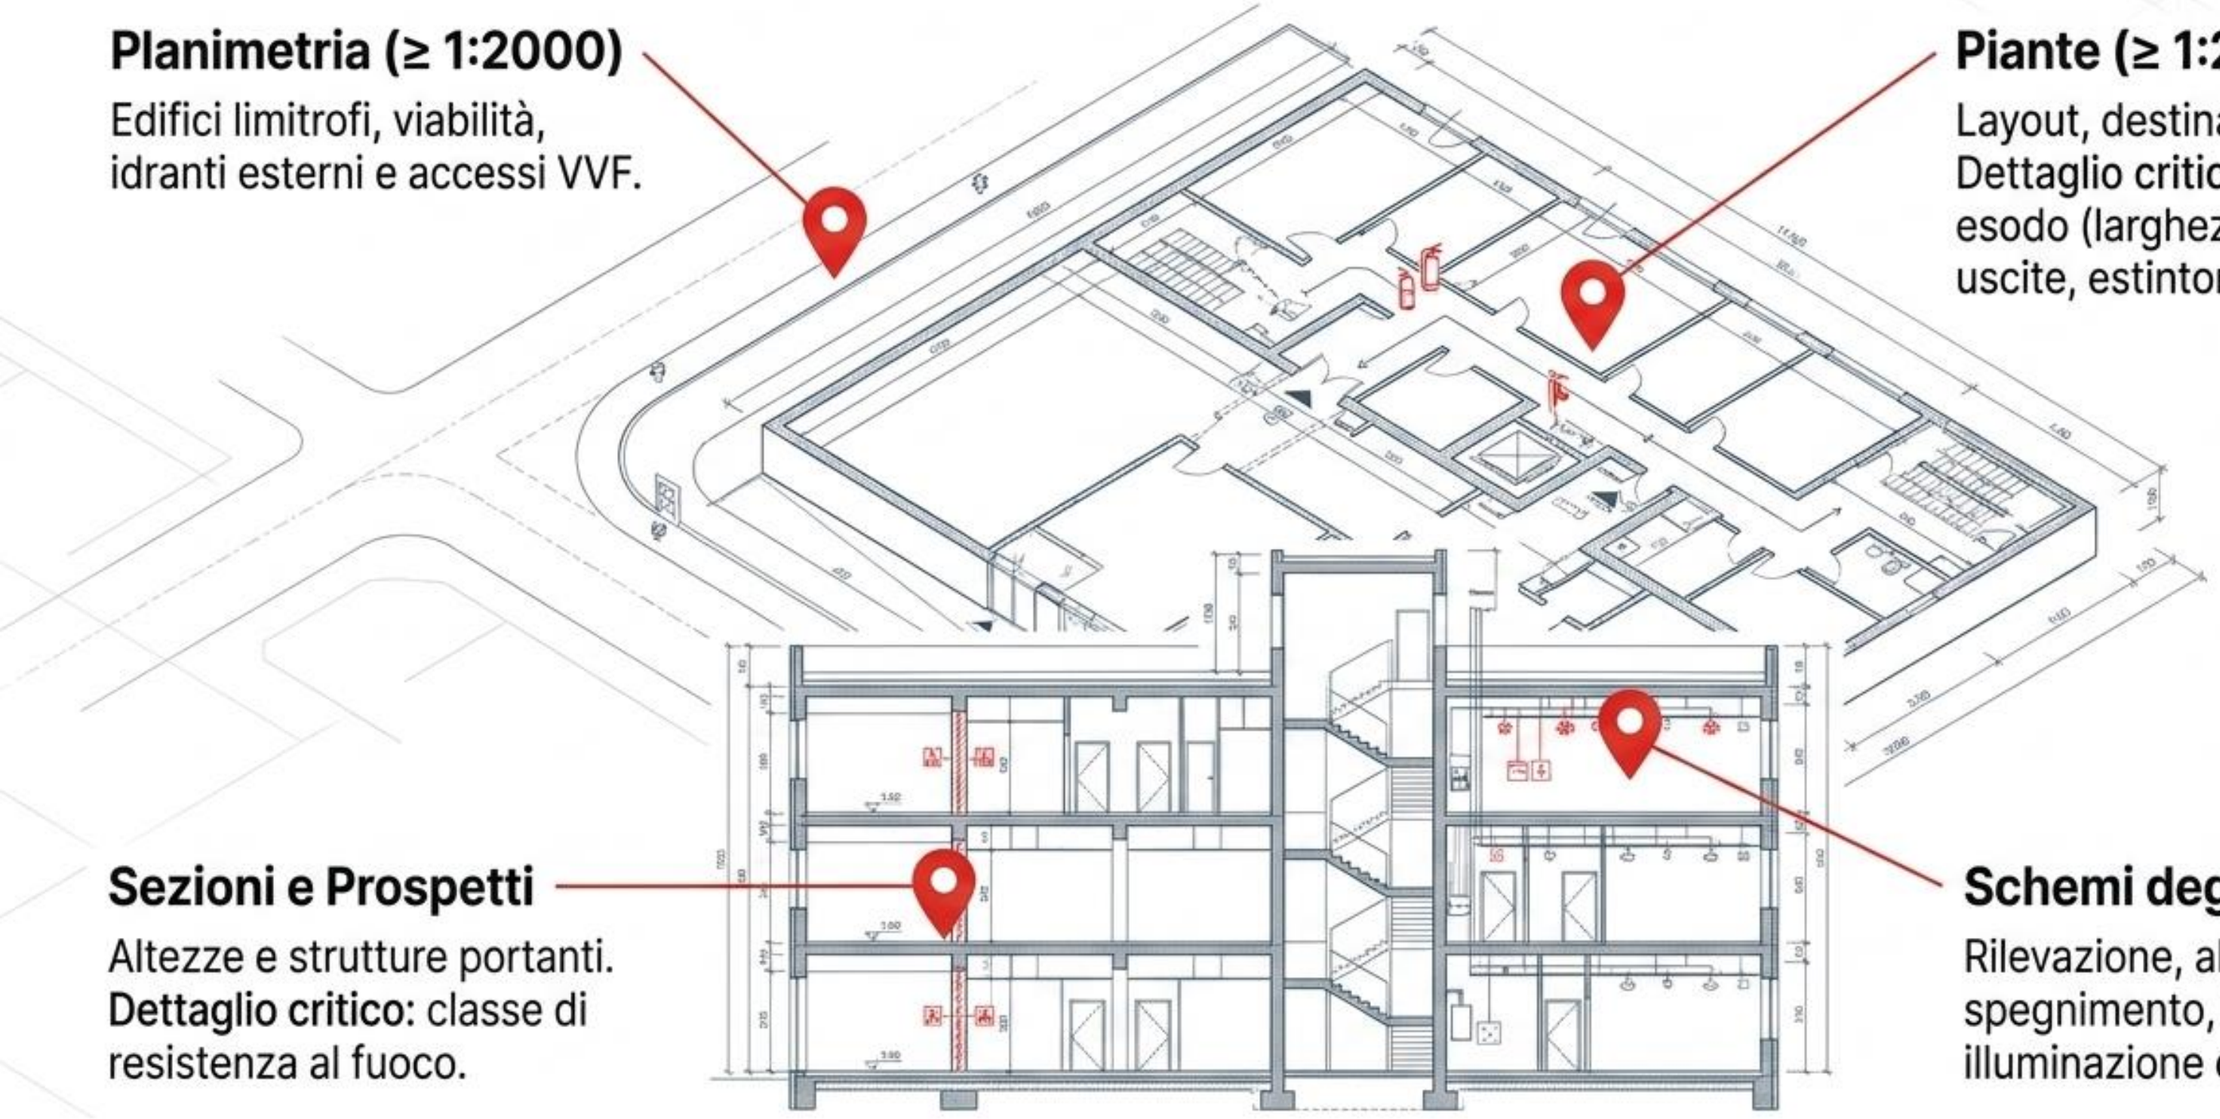

Sezioni e Prospetti

Altezze e strutture portanti. **Dettaglio critico**: classe di resistenza al fuoco.

Schemi degli Impianti

Rilevazione, allarme, spegnimento, EFC e illuminazione d'emergenza.

NotebookLM

PIN 2 – SCIA: Il Passaggio all'Esercizio

Segnalazione Certificata di Inizio Attività

La prova che la realtà costruttiva coincide con il progetto approvato.

PIN 2.1
Asseverazione del Professionista

PIN 2.2
Certificazioni Strutture REI

D.M. 37/08
Dichiarazioni Conformità Impianti

PIN 2.3
Dichiarazioni Prodotti/Materiali

NotebookLM

Il Ruolo del Professionista (PIN 2.1)

Cosa dichiara il Tecnico Abilitato (ex L. 818/1984)


- **Conformità Architettonica:** L'opera è conforme al progetto approvato (per categorie B e C).
- **Conformità Normativa:** Rispetto integrale delle norme di prevenzione incendi vigenti.
- **Efficienza Impiantistica:** Corretta installazione e perfetto funzionamento degli impianti di protezione.
- **Qualità dei Materiali:** Assoluta idoneità dei materiali e dei prodotti impiegati nella costruzione.



NotebookLM

Certificazione Strutturale REI (PIN 2.2)

Dimostrazione della classe di resistenza al fuoco (es. REI 60, REI 120)
Dimostrazione della classe di resistenza al fuoco (es. REI 60, REI 120) per elementi portanti/separanti.

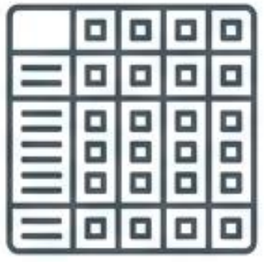

Metodo Tabellare

Riferimento diretto alle tabelle del D.M. 16 febbraio 2007.

Vantaggio: Rapido, normato, ma rigido.



Metodo Analitico

Calcoli strutturali avanzati secondo Eurocodici o norme UNI.

Vantaggio: Flessibile, ottimizzato per geometrie complesse.




Metodo Sperimentale

Rapporti di prova e certificati emessi da laboratori autorizzati.

Vantaggio: Inoppugnabile, basato su test fisici reali.

NotebookLM

Il Cuore Attivo: Gli Impianti (D.M. 37/2008)

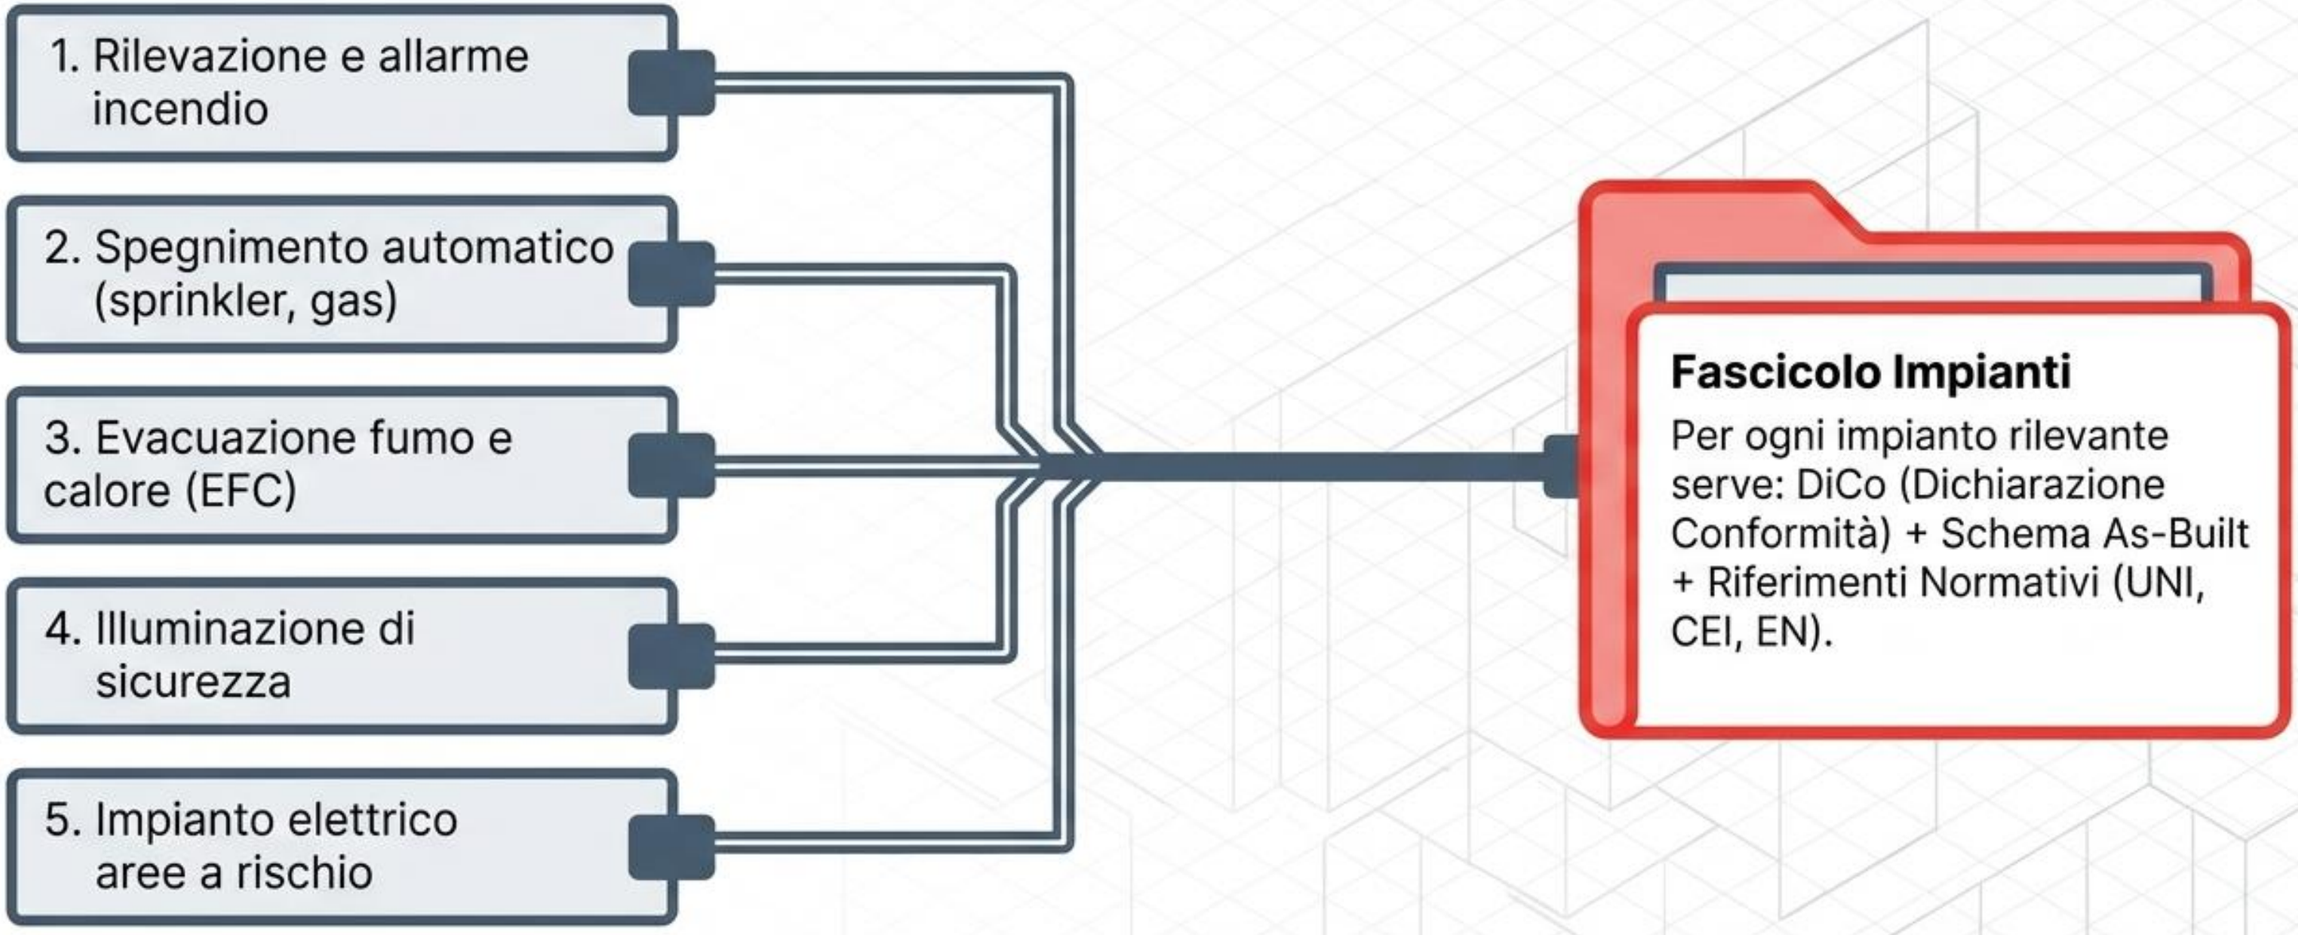

NotebookLM

Il Controllo dei Materiali & Documenti Integrativi



Ulteriore Documentazione

- Certificato di collaudo (impianti protezione attiva)
- Registro dei controlli periodici (ove previsto)
- Piano di emergenza con procedure di evacuazione
- Documentazione fotografica dello stato dei luoghi

NotebookLM

PIN 3 – Il Ciclo di Vita (Rinnovo Periodico)

1. Il Responsabile


Dichiara formalmente che le condizioni di sicurezza originali non sono mutate nel tempo.

2. I Documenti

Presentazione dell'elenco degli interventi di manutenzione effettuati ed eventuali aggiornamenti tecnici.

3. Il Tecnico

Fornisce l'asseverazione tecnica a garanzia della continuità prestazionale.

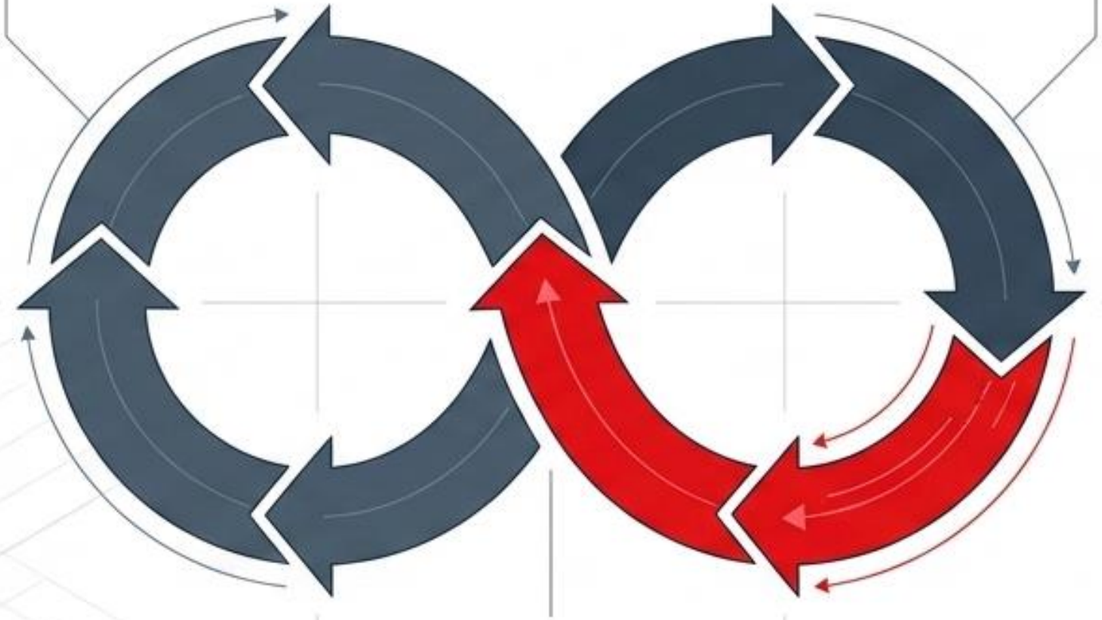

NotebookLM